


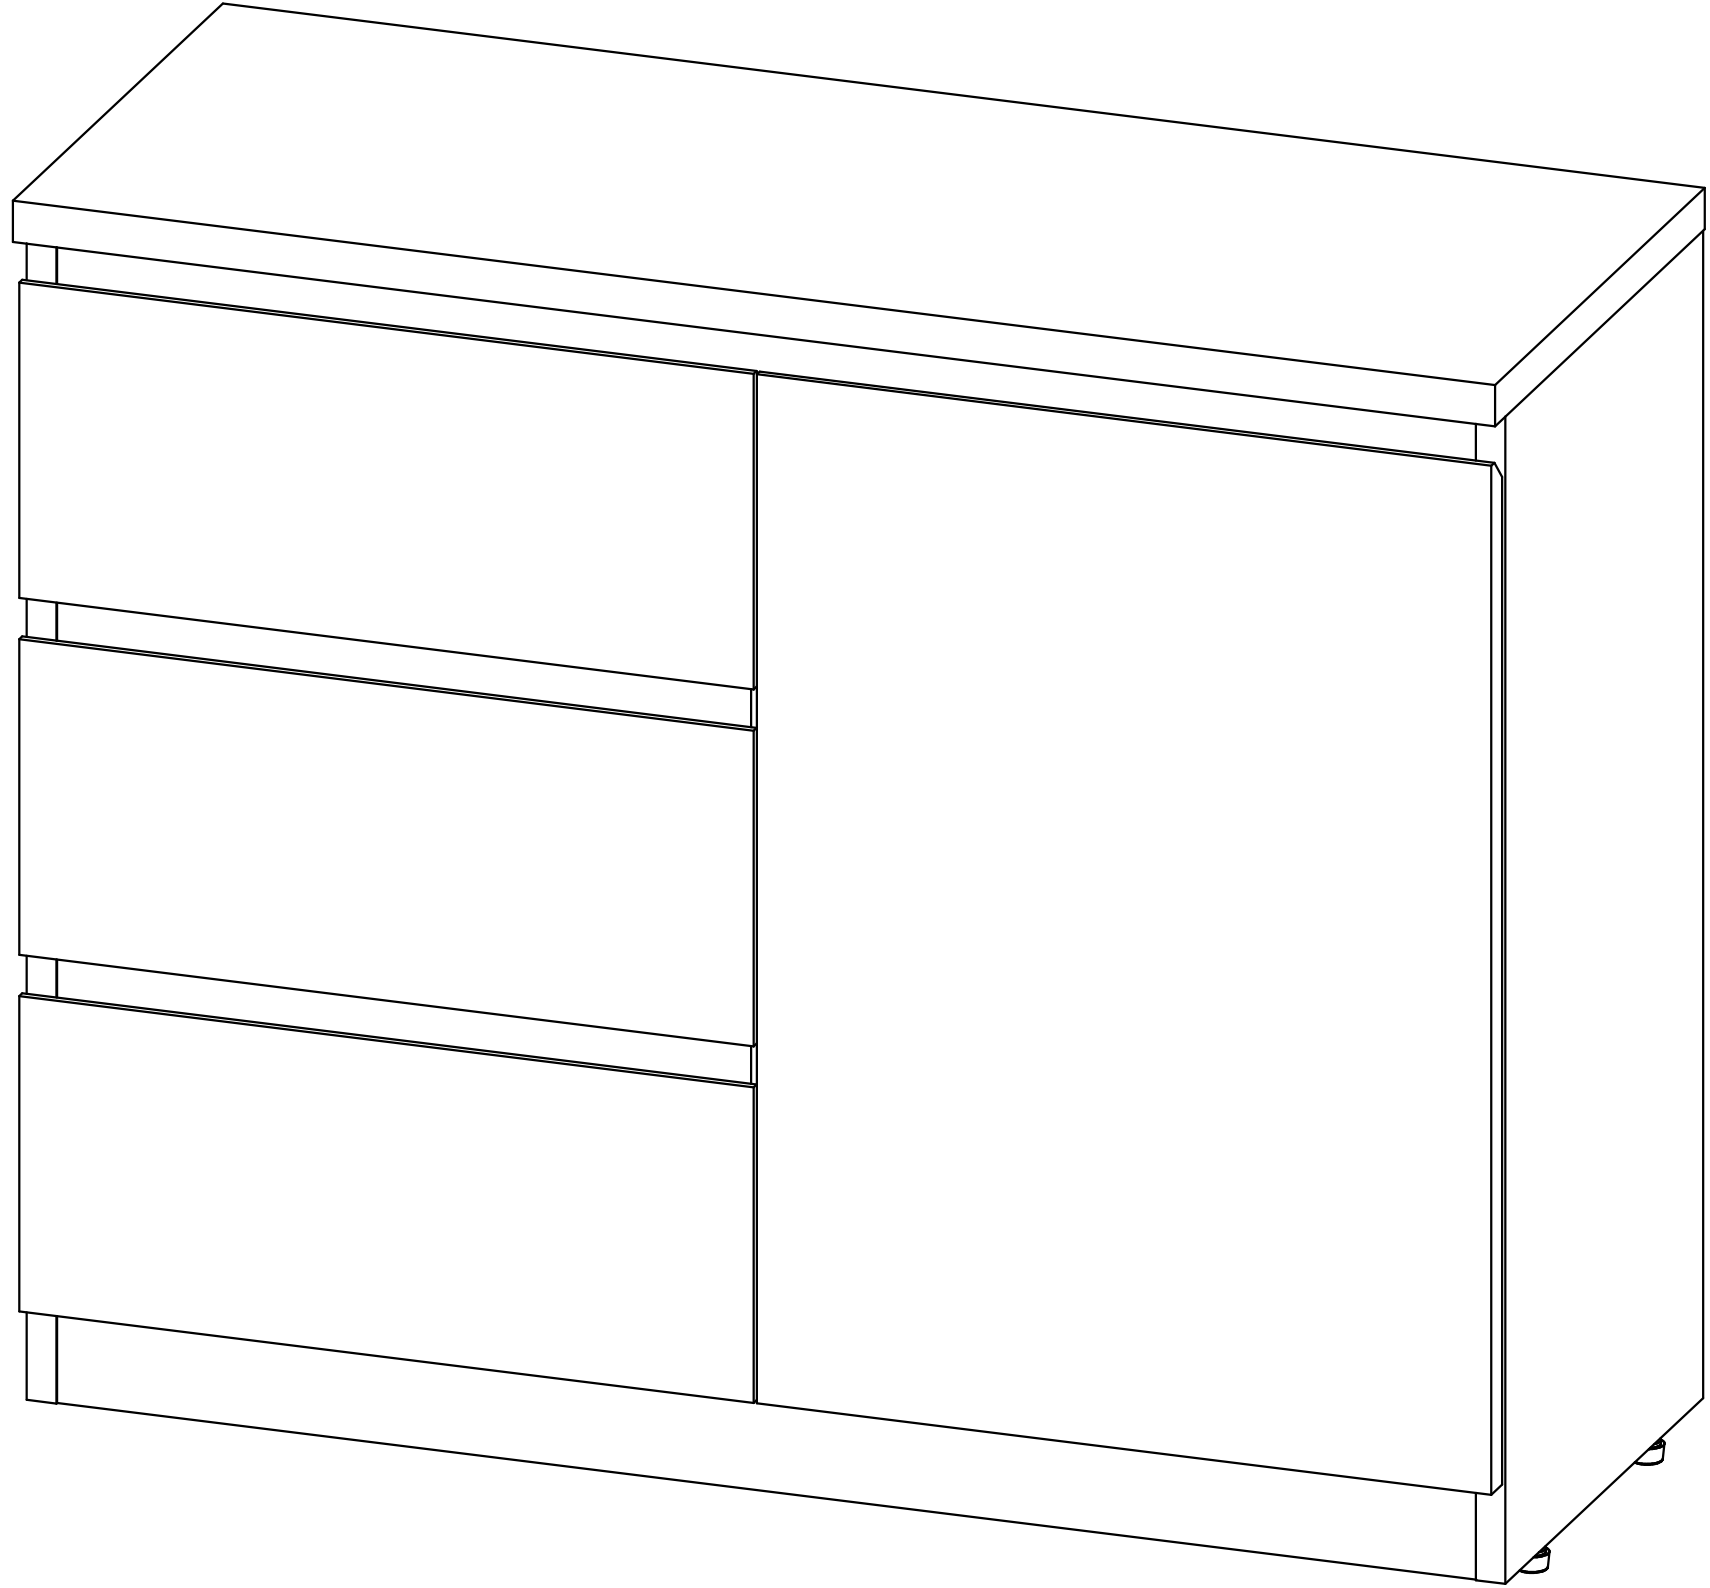


Bảng thống kê tấm chi tiết và thanh

Đơn hàng TỦ THẤP (900X350X750)

Sản phẩm MBCN ...

Mã sản phẩm

CT.	Tên	Mã	Chi tiết chưa dán cạnh		Slg.	W1	W2	D1	D2
			Dài	Rộng					
1	NOC TU	O25M1M2	898	348	1	NEP1X28M1	NEP1X28M1	NEP1X28M1	NEP1X28M1
2	DAY TU	O17M1M2	862	328	1	NEP1X21M1	NEP1X21M1		
3	CANH TU	O17M1M2	623	444	1	NEP1X21M1	NEP1X21M1	NEP1X28M1	NEP1X21M1
4	THANH TU	O17M1M2	709	328	1	NEP1X21M1	NEP1X21M1		NEP1X21M1
5	THANH TU	O17M1M2	709	328	1	NEP1X21M1	NEP1X21M1		NEP1X21M1
6	VACH TU	O17M1M2	632	311	1		NEP1X21M1		
7	DOT M	O17M1M2	420	301	1	NEP1X21M1			NEP1X21M1
8	CANH TU	O17M1M2	190	444	3	NEP1X21M1	NEP1X21M1	NEP1X28M1	NEP1X21M1
9	CHAN CON	O17M1M2	59	862	3				NEP1X21M1
10	TNK	O17M1M2	361	102	3		NEP1X21M1		
11	TNK	O17M1M2	361	102	3		NEP1X21M1		
12	TNK	O17M1M2	299	119	3	NEP1X21M1	NEP1X21M1	NEP1X21M1	
13	TNK	O17M1M2	299	119	3	NEP1X21M1	NEP1X21M1	NEP1X21M1	
14	CHAN CON	O17M1M2	58	422	2			NEP1X21M1	NEP1X21M1
15	HAU 6	M5.5M1M2	642	872	1				
16	DNK	M5.5M1M2	381	300	3				

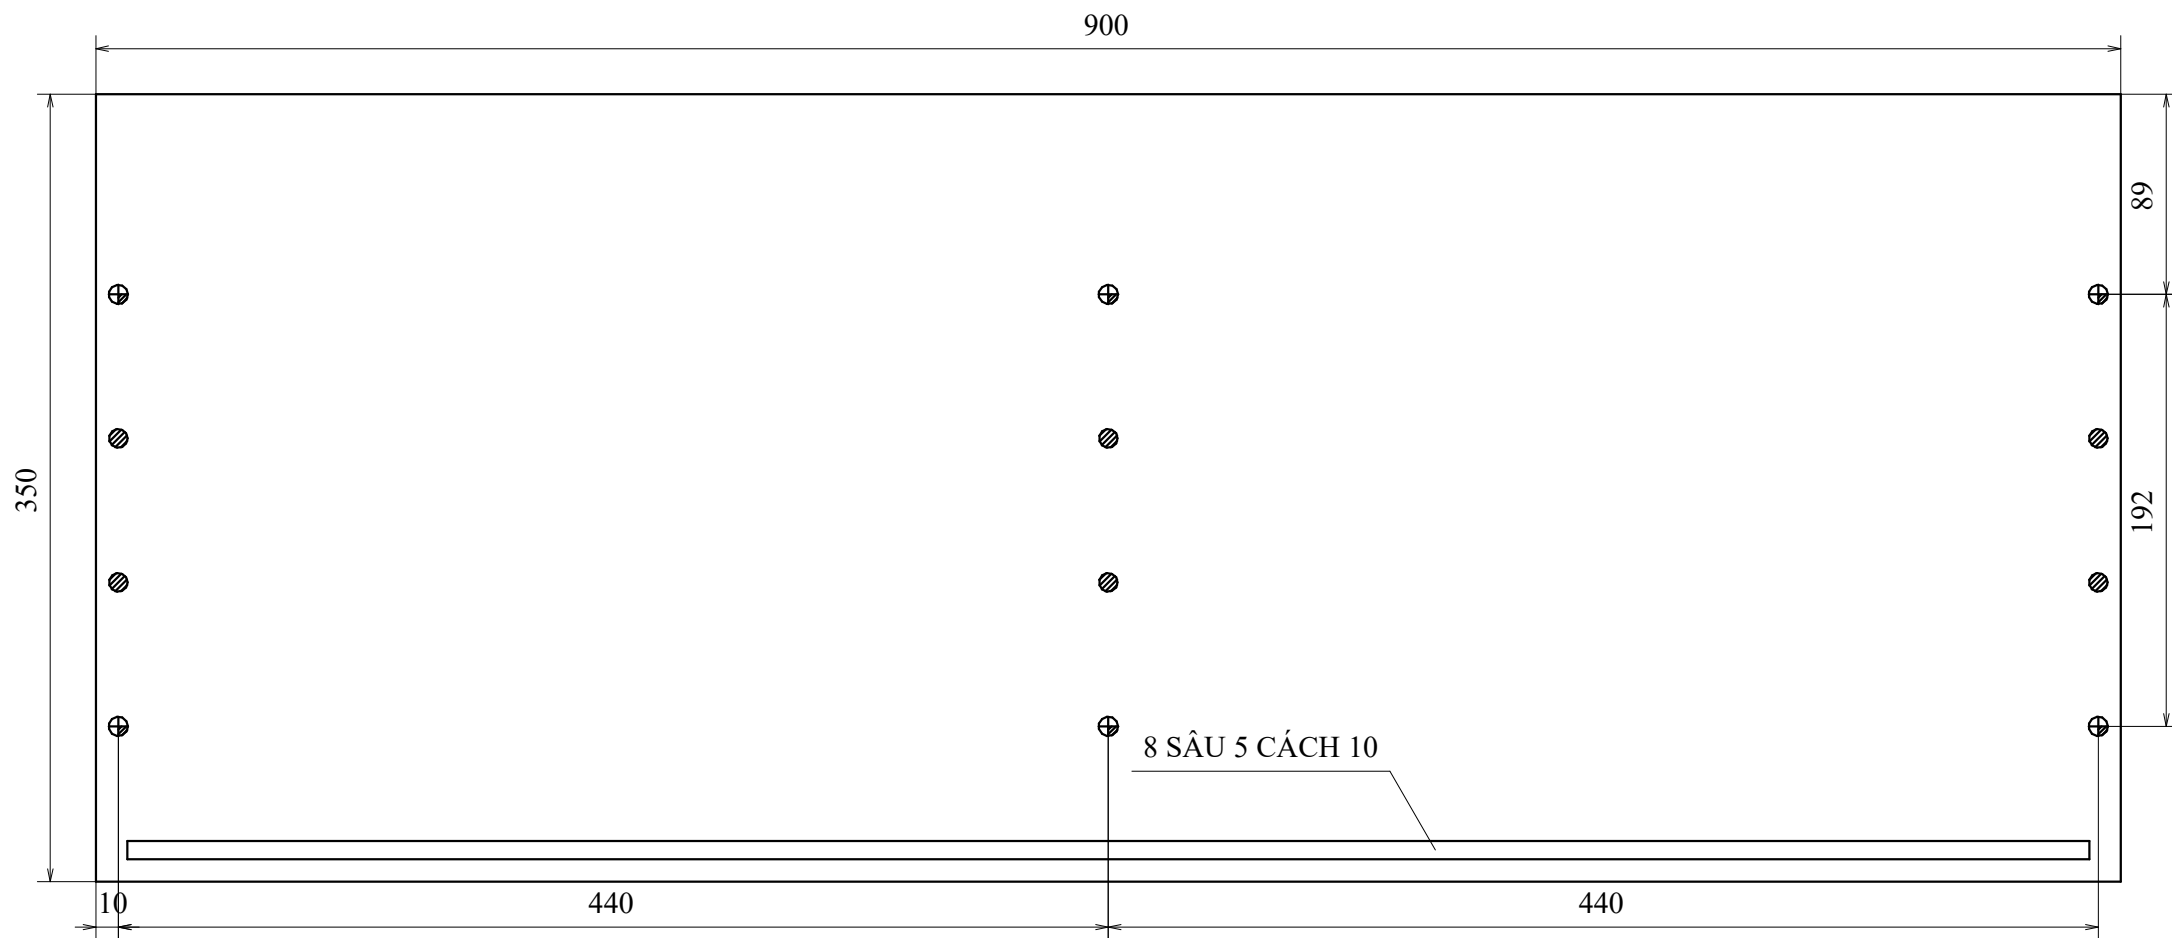

1 . NOC TU .SL: 1

Ghi chú

- Ø15 SÂU 13
- ⊗ Ø8 SÂU 13 (MẶT)
- ⊗ Ø8 SÂU 25 (CẠNH)
- ⊗ Ø5 THÙNG

- ⊗ Ø8 THÙNG
- ⊗ Ø8 THÙNG
- ⊗ Ø5 SÂU 13

Dung sai tổng thể ± 5mm

TỦ THẤP (900X350X750)

		Chữ ký	Ngày
Thiết kế	Phạm Huân		07.06.21
Kiểm soát	Văn Nam		
Duyệt			


BẢN VẼ

Vật liệu: OKAL-M1

MBCN ...


Số lượng		

HÒA PHÁT
NHÀ MÁY GỖ HÒA PHÁT

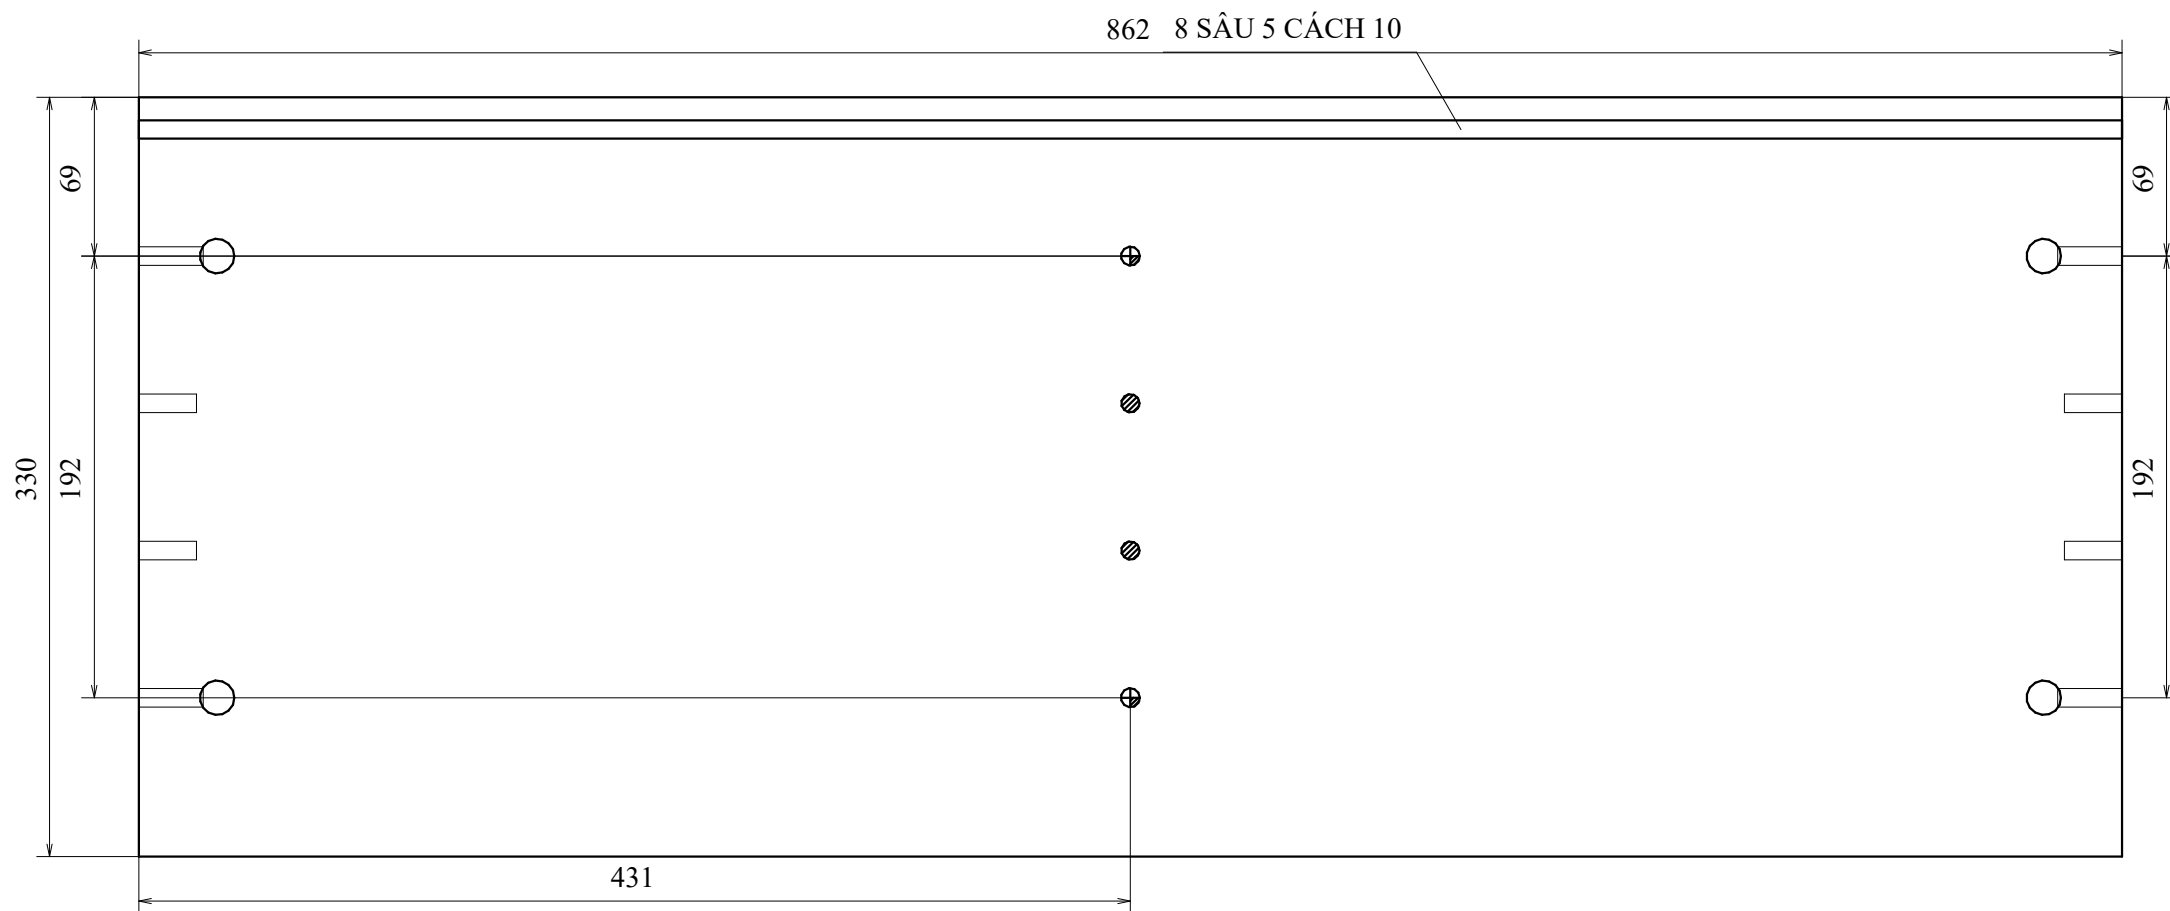


2 . DAY TU .SL: 1

Ghi chú		TỦ THẤP (900X350X750)								
○ Ø15 SẤU 13 ⊘ Ø8 SẤU 13 (MẶT) ⊘ Ø8 SẤU 25 (CẠNH) ⊗ Ø5 THÙNG ⊗ Ø8 THÙNG ⊗ Ø8 THÙNG ⊕ Ø5 SẤU 13						BẢN VẼ	MBCN ...			
								Số lượng		
		Thiết kế	Phạm Huân		Chữ ký		Ngày			
							07.06.21			
		Kiểm soát	Văn Nam							
Dung sai tổng thể ± 5mm		Duyệt				Vật liệu: OKAL-MI	HÒA PHÁT HỘI THAY NHÀ MÁY GỖ HÒA PHÁT			

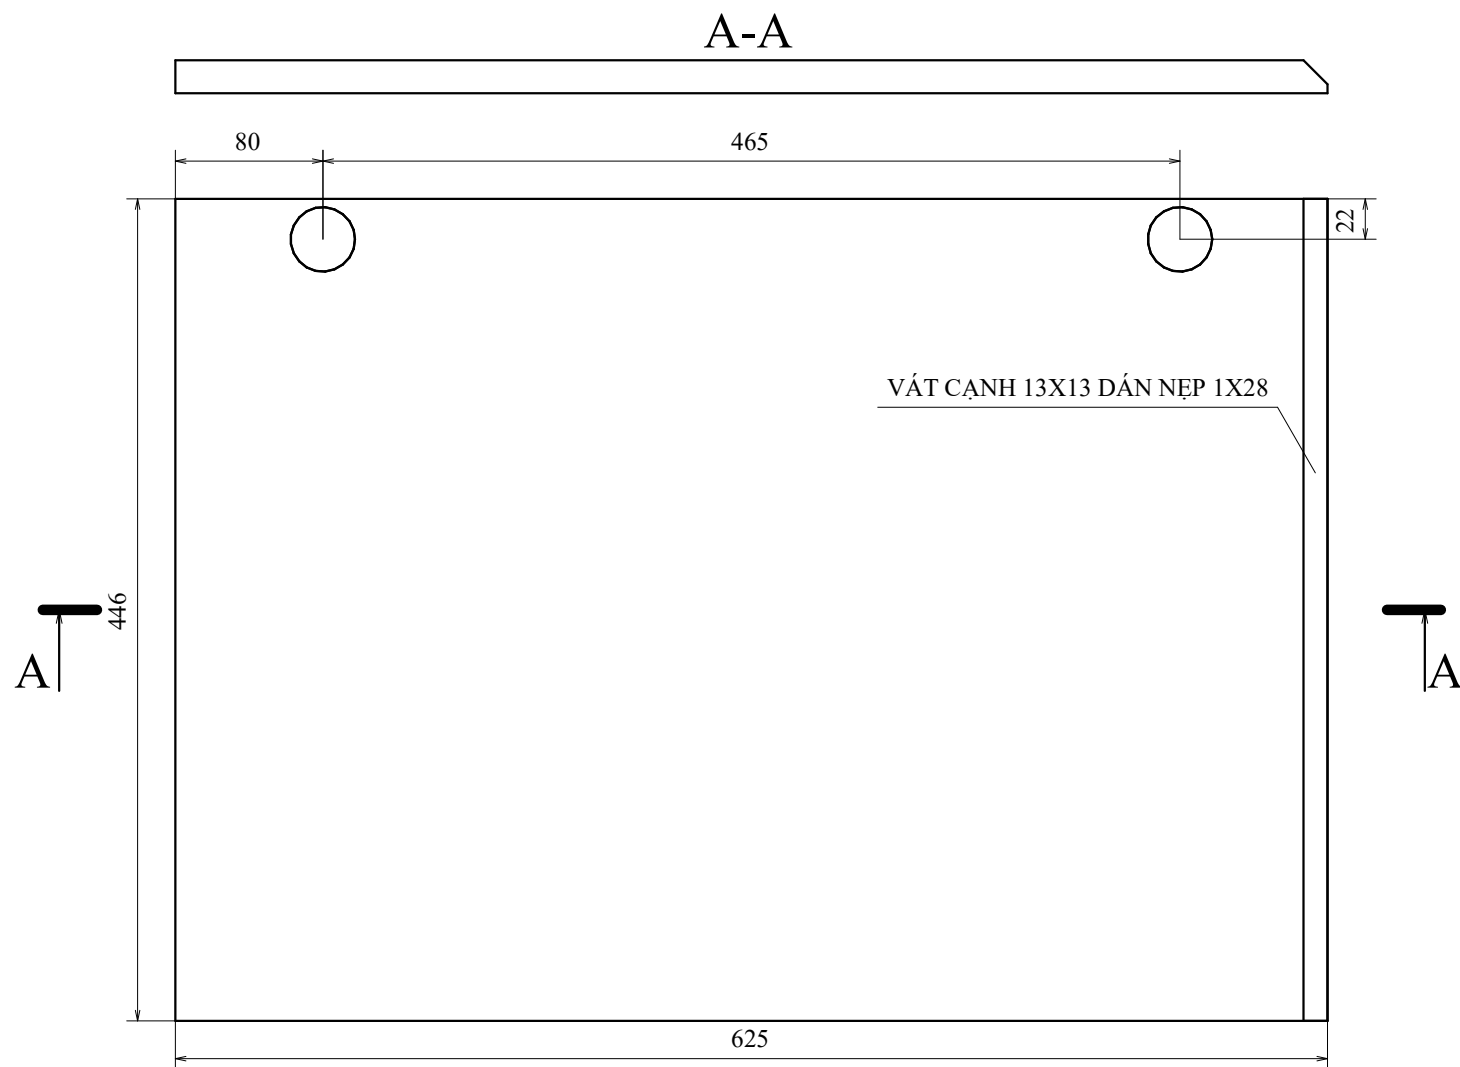

3 . CẠNH TỦ .SL: 1

Ghi chú		TỦ THẤP (900X350X750)								
○ Ø15 SẤU 13 ⊘ Ø8 SẤU 13 (MẶT) ⊘ Ø8 SẤU 25 (CẠNH) ⊗ Ø5 THÙNG	⊗ Ø8 THÙNG ⊗ Ø8 THÙNG ⊕ Ø5 SẤU 13					BẢN VẼ	MBCN ...			
								Số lượng		
		Thiết kế	Phạm Huân	Chữ ký	Ngày					
		Kiểm soát	Văn Nam							
Dung sai tổng thể ± 5mm		Duyệt				Vật liệu: OKAL-MI	HOA PHAT HUY THAT NHÀ MÁY GỖ HOA PHẤT			

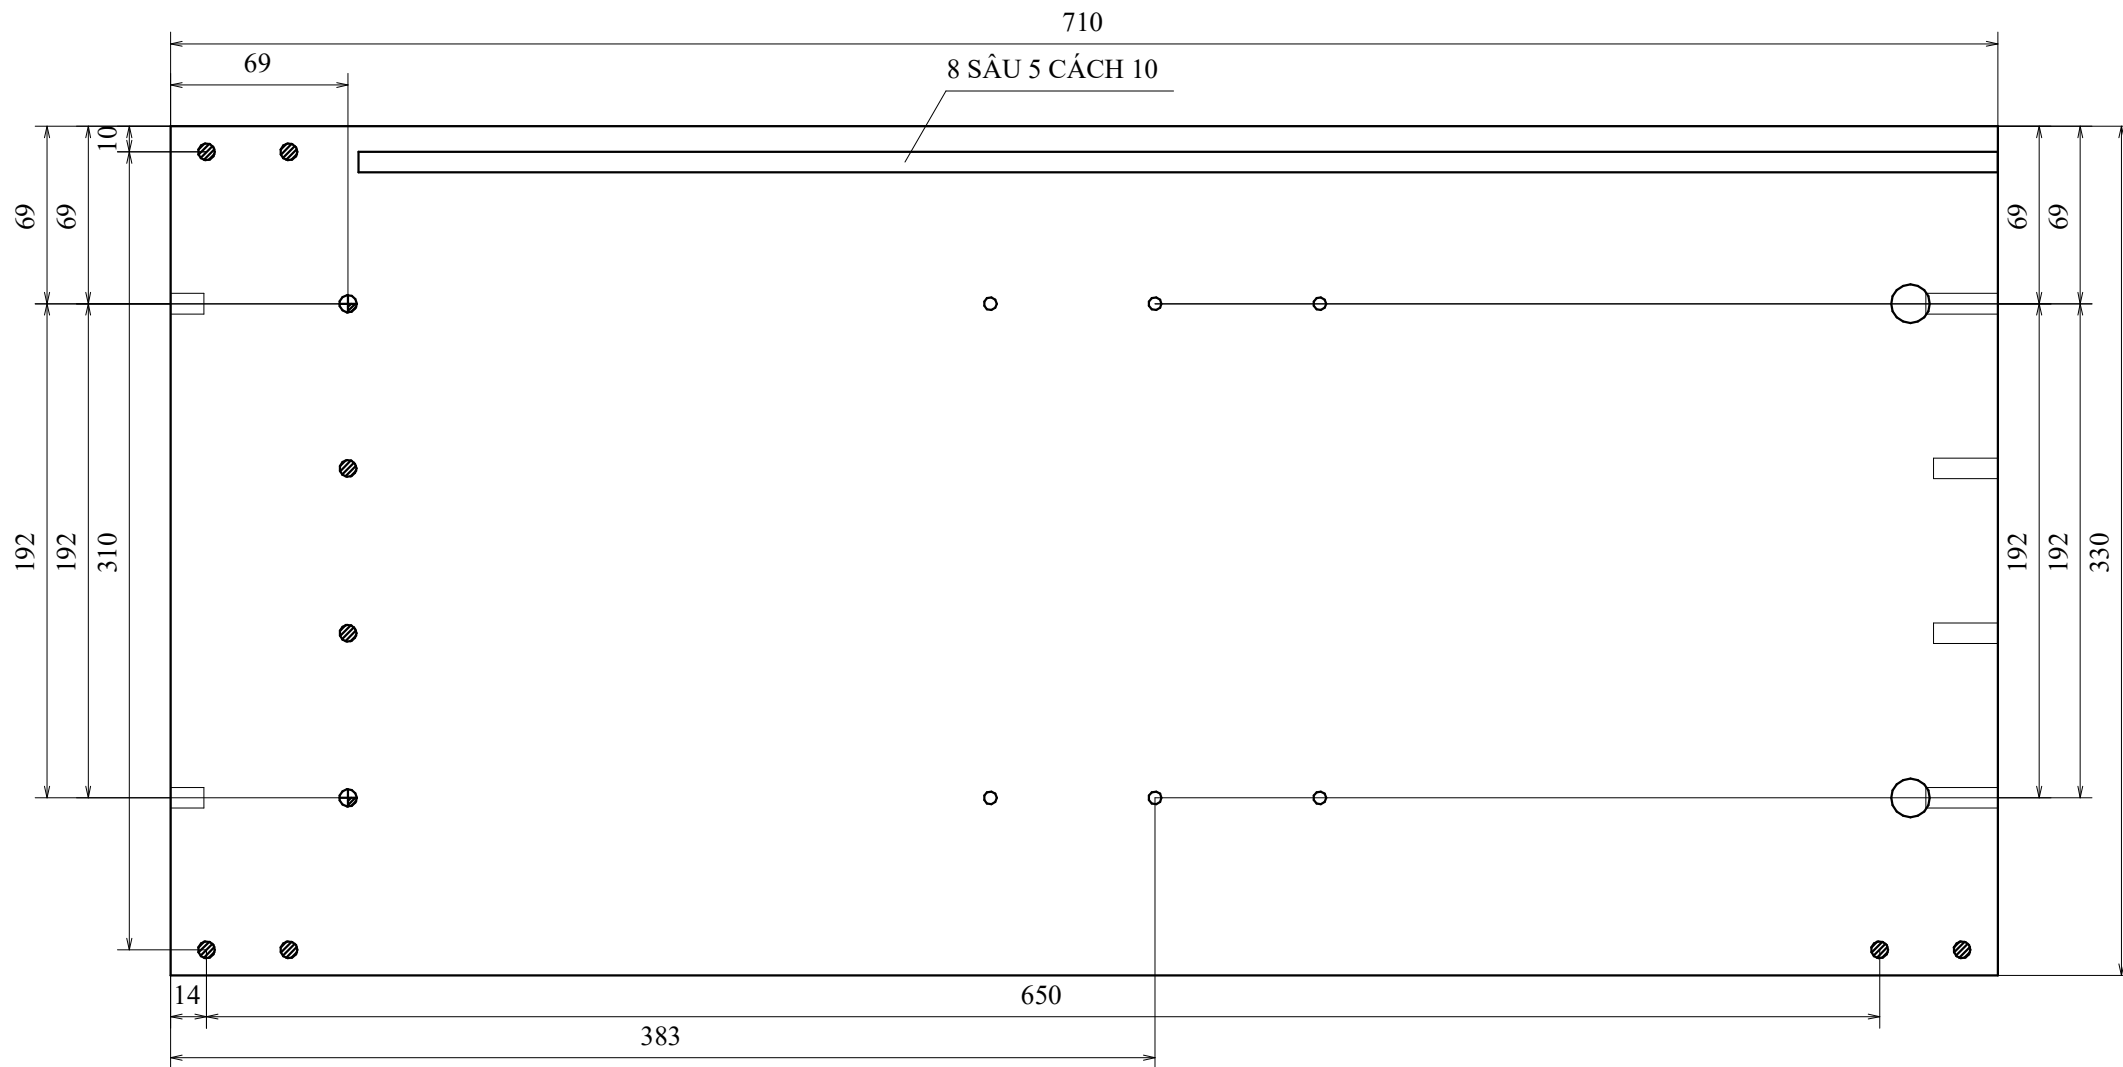

4 . THANH TU .SL: 1

Ghi chú

- Ø15 SÂU 13
- ⊗ Ø8 SÂU 13 (MẶT)
- ⊗ Ø8 SÂU 25 (CẠNH)
- ⊗ Ø5 THÙNG

- ⊗ Ø8 THÙNG
- ⊗ Ø8 THÙNG
- ⊗ Ø5 SÂU 13

Dung sai tổng thể ± 5mm

TỦ THẤP (900X350X750)

		Chữ ký	Ngày
Thiết kế	Phạm Huân		07.06.21
Kiểm soát	Văn Nam		
Duyệt			


BẢN VẼ

Vật liệu: OKAL-M1

MBCN ...

Số lượng

HÒA PHÁT
NHÀ MÁY GỖ HÒA PHÁT

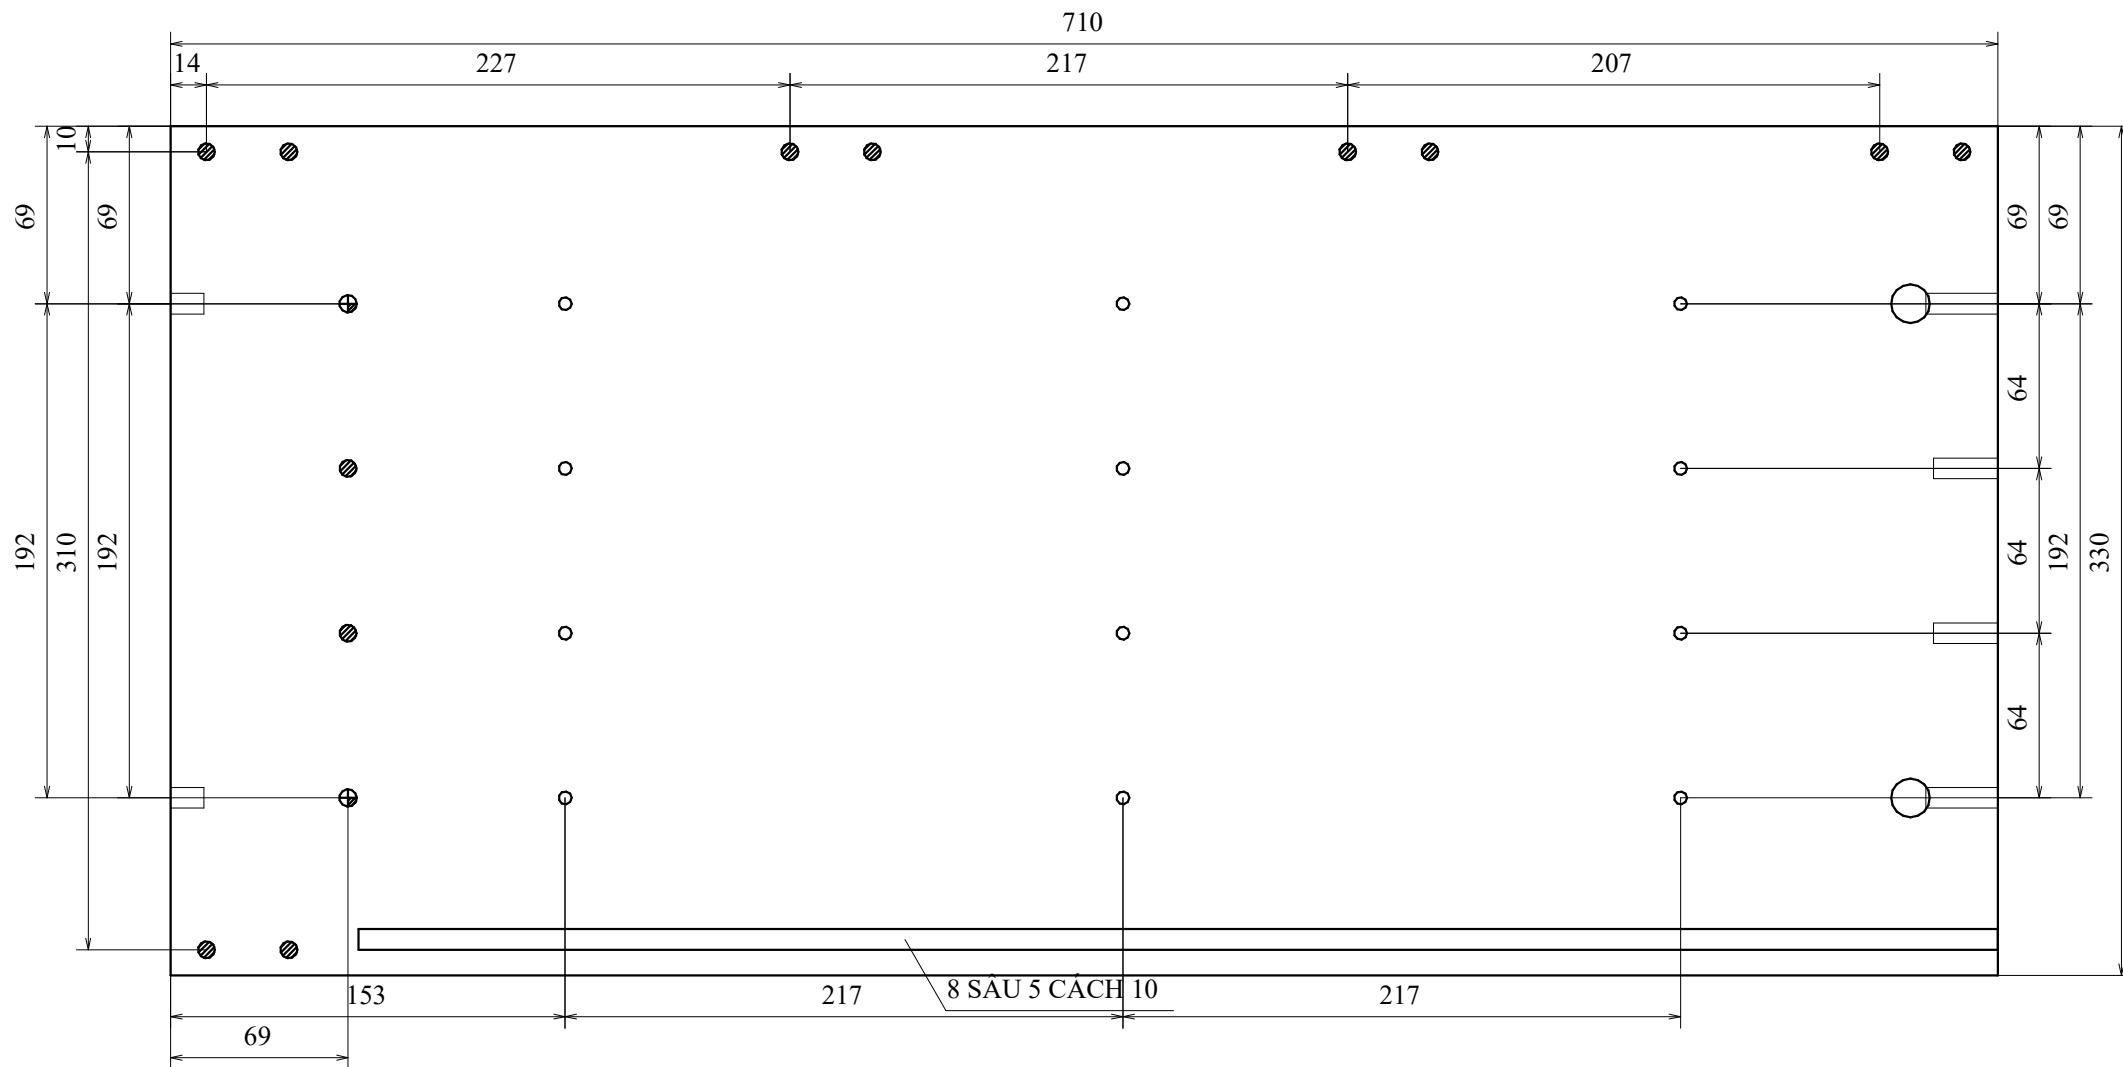

5 . THANH TU .SL: 1

Ghi chú

- Ø15 SẤU 13
- ⊗ Ø8 SẤU 13 (MẶT)
- ⊗ Ø8 SẤU 25 (CẠNH)
- ⊗ Ø5 THÙNG

- ⊗ Ø8 THÙNG
- ⊗ Ø8 THÙNG
- ⊗ Ø5 SẤU 13

Dung sai tổng thể $\pm 5mm$

TỦ THẤP (900X350X750)

		Chữ ký	Ngày
Thiết kế	Phạm Huân		07.06.21
Kiểm soát	Văn Nam		
Duyệt			


BẢN VẼ

Vật liệu: OKAL-M1

MBCN ...


Số lượng

HÒA PHÁT
NHÀ MÁY GỖ HÒA PHÁT

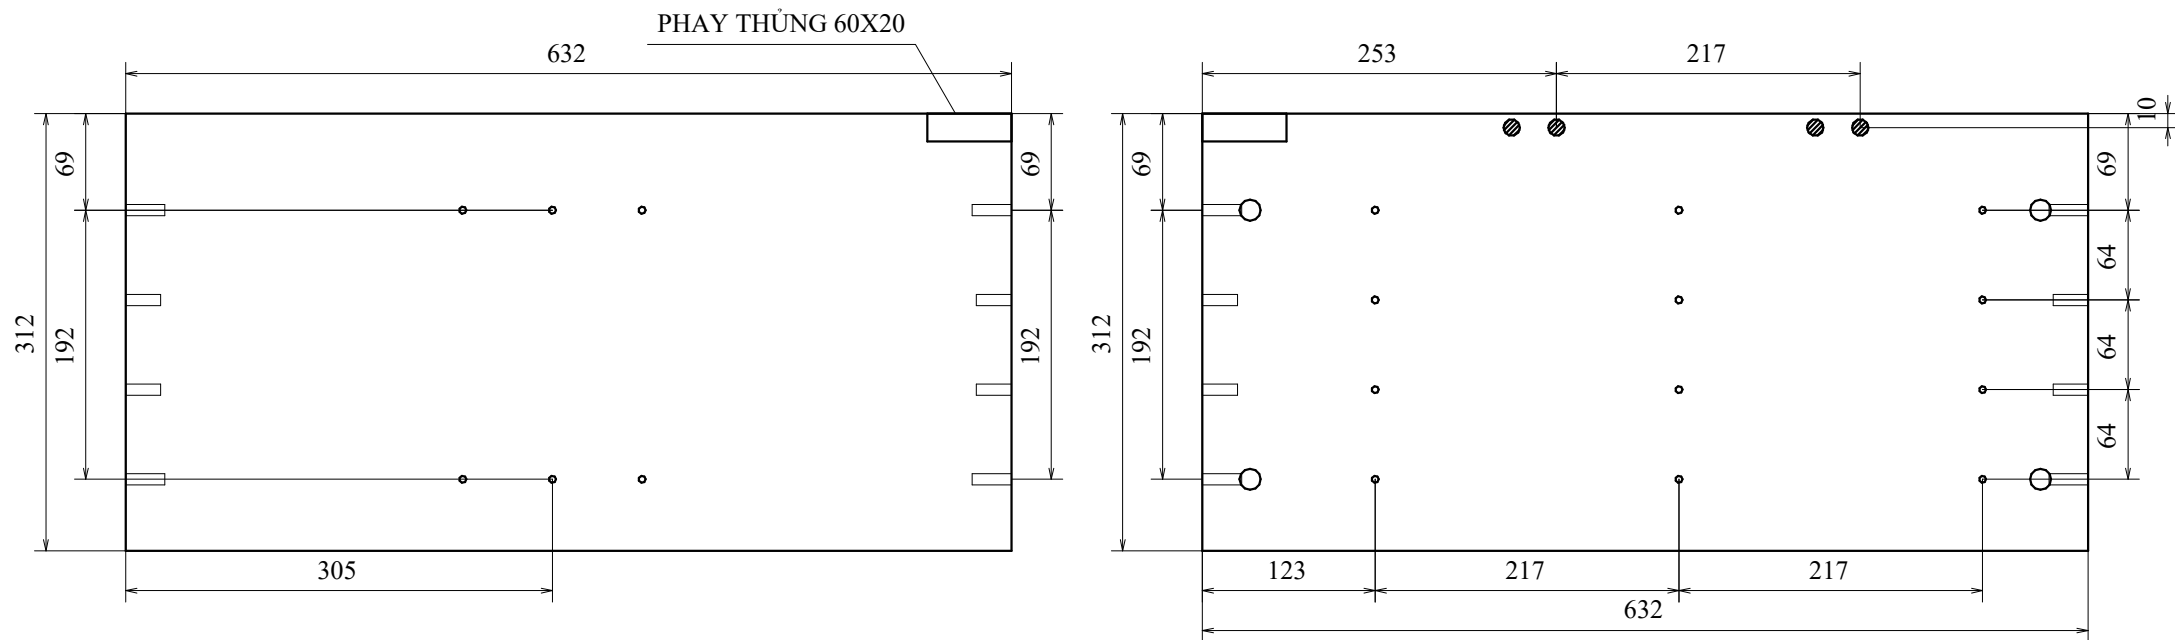

6 . VACH TU .SL: 1

Ghi chú		TỦ THẤP (900X350X750)								
○ Ø15 SẤU 13 ⊘ Ø8 SẤU 13 (MẶT) ⊘ Ø8 SẤU 25 (CẠNH) ⊗ Ø5 THÙNG ⊗ Ø8 THÙNG ⊗ Ø8 THÙNG ⊕ Ø5 SẤU 13	Dung sai tổng thể ± 5mm					BẢN VẼ	MBCN ...			
								Số lượng		
		Thiết kế	Phạm Huân	Chữ ký	Ngày					
		Kiểm soát	Văn Nam							
								Vật liệu: OKAL-MI	HOA PHAT HỘI THẤT NHÀ MÁY GỖ HOA PHÁT	

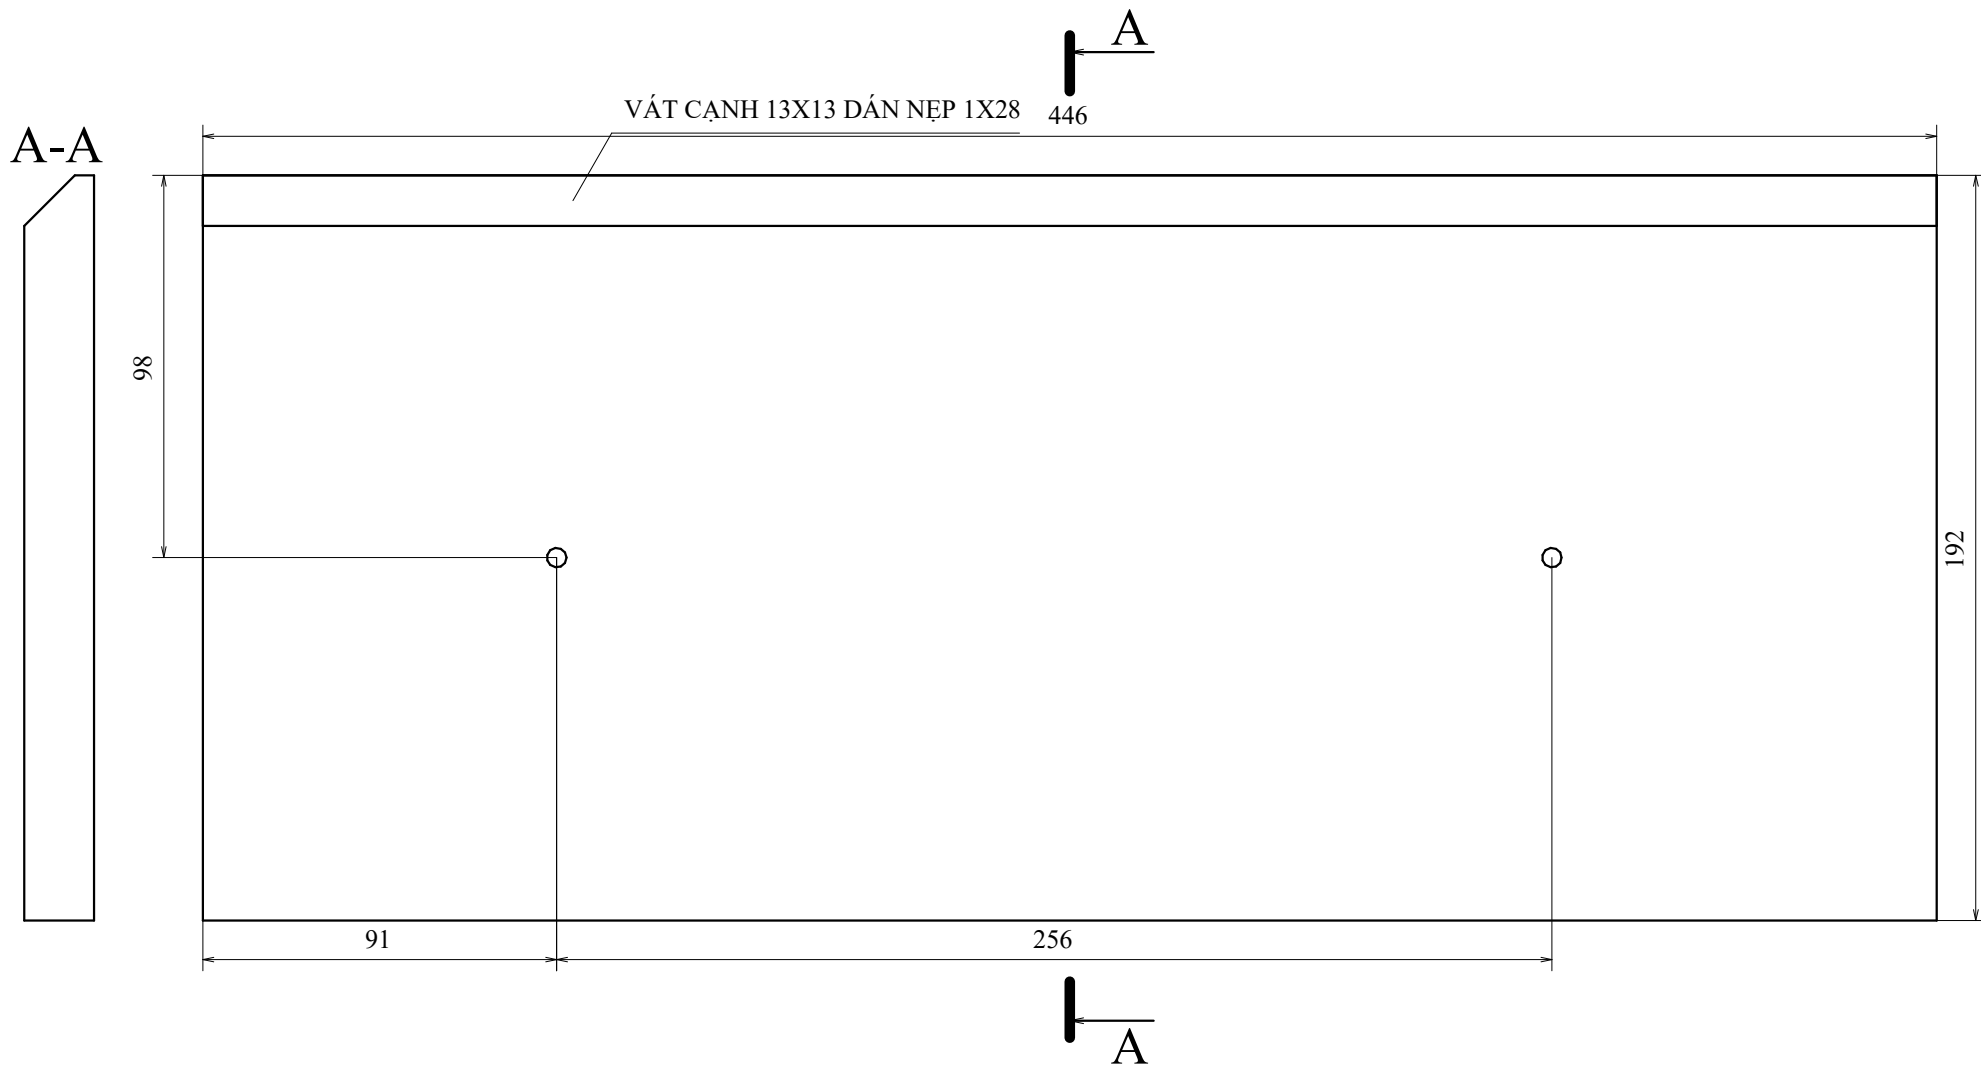

8 . CANH TU .SL: 3

Ghi chú

- Ø15 SẤU 13
- ⊘ Ø8 SẤU 13 (MẶT)
- ⊘ Ø8 SẤU 25 (CẠNH)
- ⊗ Ø5 THÙNG

- ⊙ Ø8 THÙNG
- ⊗ Ø8 THÙNG
- ⊕ Ø5 SẤU 13

Dung sai tổng thể ± 5mm

TỦ THẤP (900X350X750)

		Chữ ký	Ngày
Thiết kế	Phạm Huân		07.06.21
Kiểm soát	Văn Nam		
Duyệt			


BẢN VẼ

Vật liệu: OKAL-M1

MBCN ...


Số lượng		

HÒA PHÁT
HỘI THAY
NHÀ MÁY GỖ HÒA PHÁT

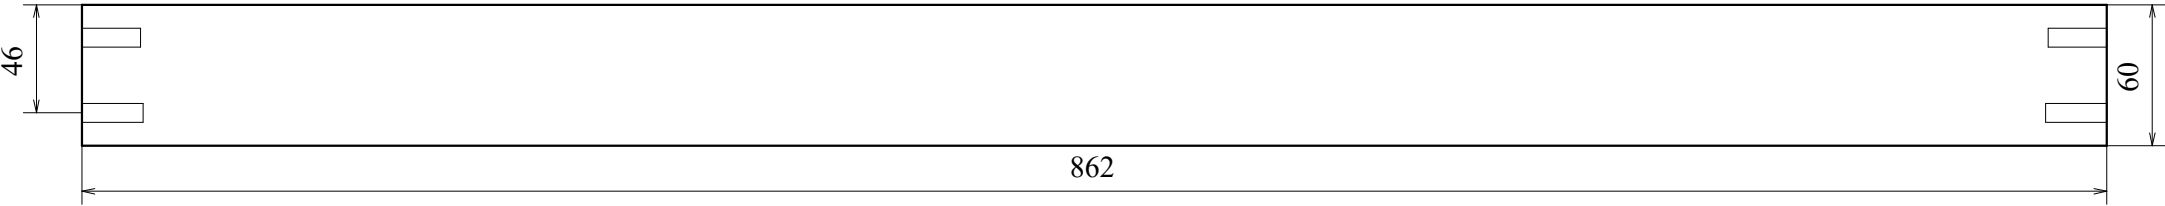


9 . CHAN CON .SL: 3


Ghi chú				TỦ THẤP (900X350X750)							
○ Ø15 SẤU 13 ⊘ Ø8 SẤU 13 (MẶT) ⊘ Ø8 SẤU 25 (CẠNH) ⊗ Ø5 THÙNG	⊗ Ø8 THÙNG ⊗ Ø8 THÙNG ⊕ Ø5 SẤU 13					BẢN VẼ	MBCN ...				
							Số lượng				
						Chữ ký	Ngày				
						Thiết kế	Phạm Huân	07.06.21			
						Kiểm soát	Văn Nam				
						Duyệt					
		Dung sai tổng thể ± 5mm						Vật liệu: OKAL-M1	 HOA PHAT HỘI THAY NHÀ MÁY GỖ HOA PHAT		

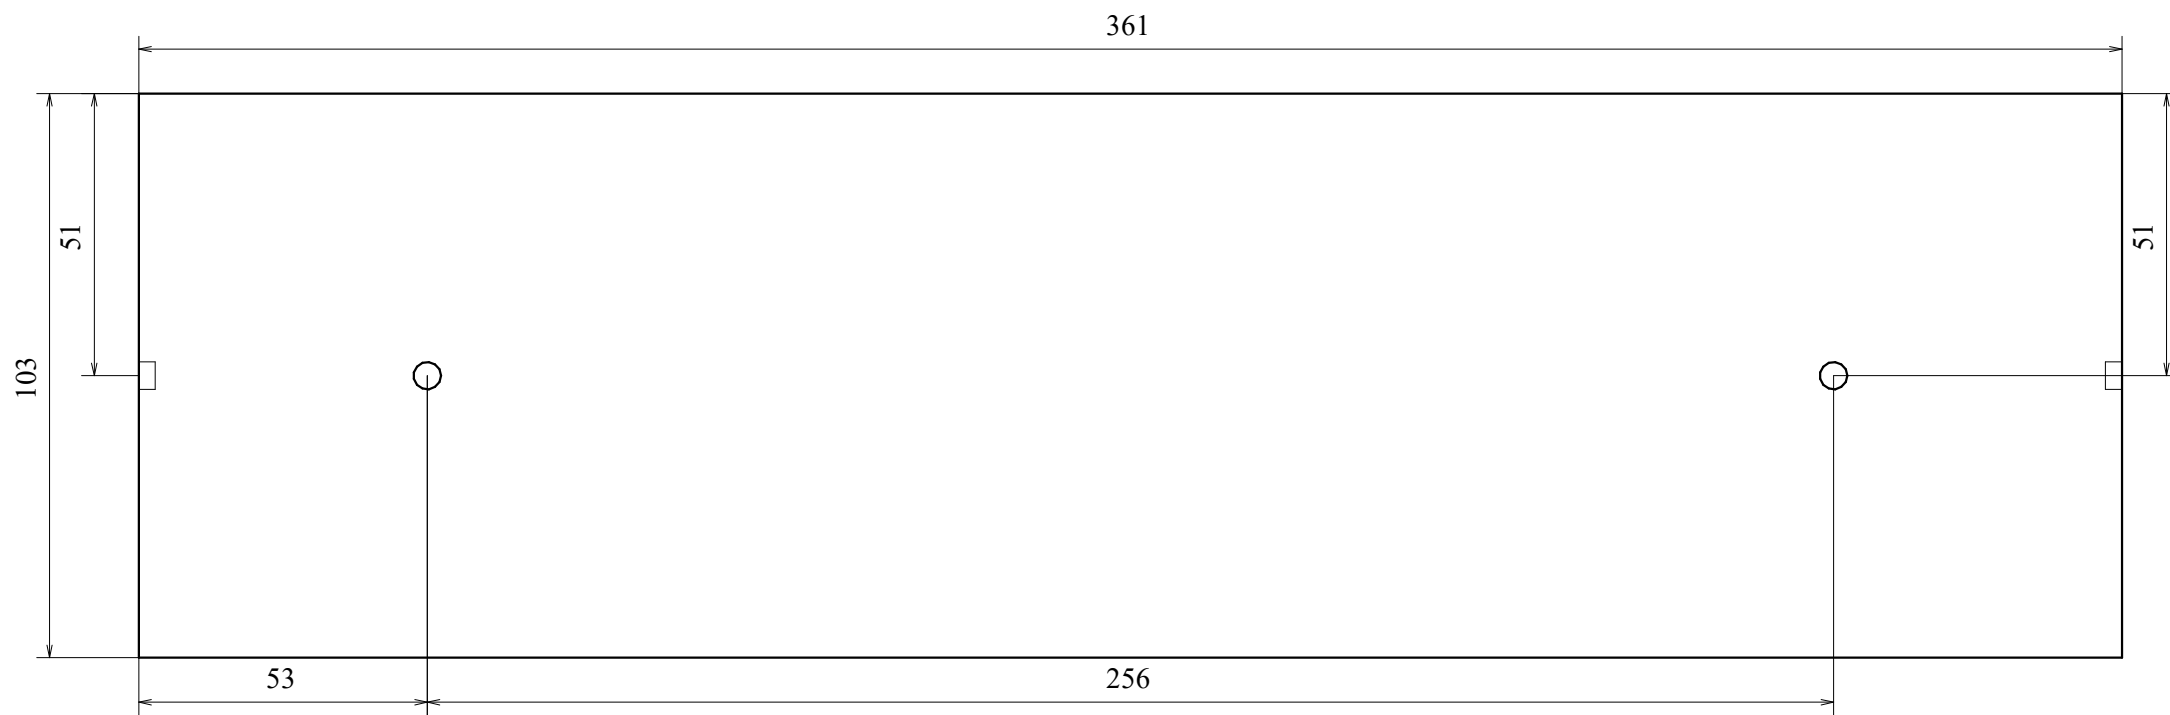

11 . TNK

.SL: 3

 Ghi chú				TỦ THẤP (900X350X750)							
○ Ø15 SẤU 13 ⊘ Ø8 SẤU 13 (MẶT) ⊘ Ø8 SẤU 25 (CẠNH) ⊗ Ø5 THÙNG ⊗ Ø8 THÙNG ⊗ Ø8 THÙNG ⊕ Ø5 SẤU 13		Dung sai tổng thể ± 5mm						BẢN VẼ	MBCN ...		
									Số lượng		
						Chữ ký	Ngày				
				Thiết kế	Phạm Huân		07.06.21				
				Kiểm soát	Văn Nam						
				Duyệt				Vật liệu: OKAL-MI	HOA PHAT HOI THAY NHÀ MÁY GỖ HOA PHÁT		

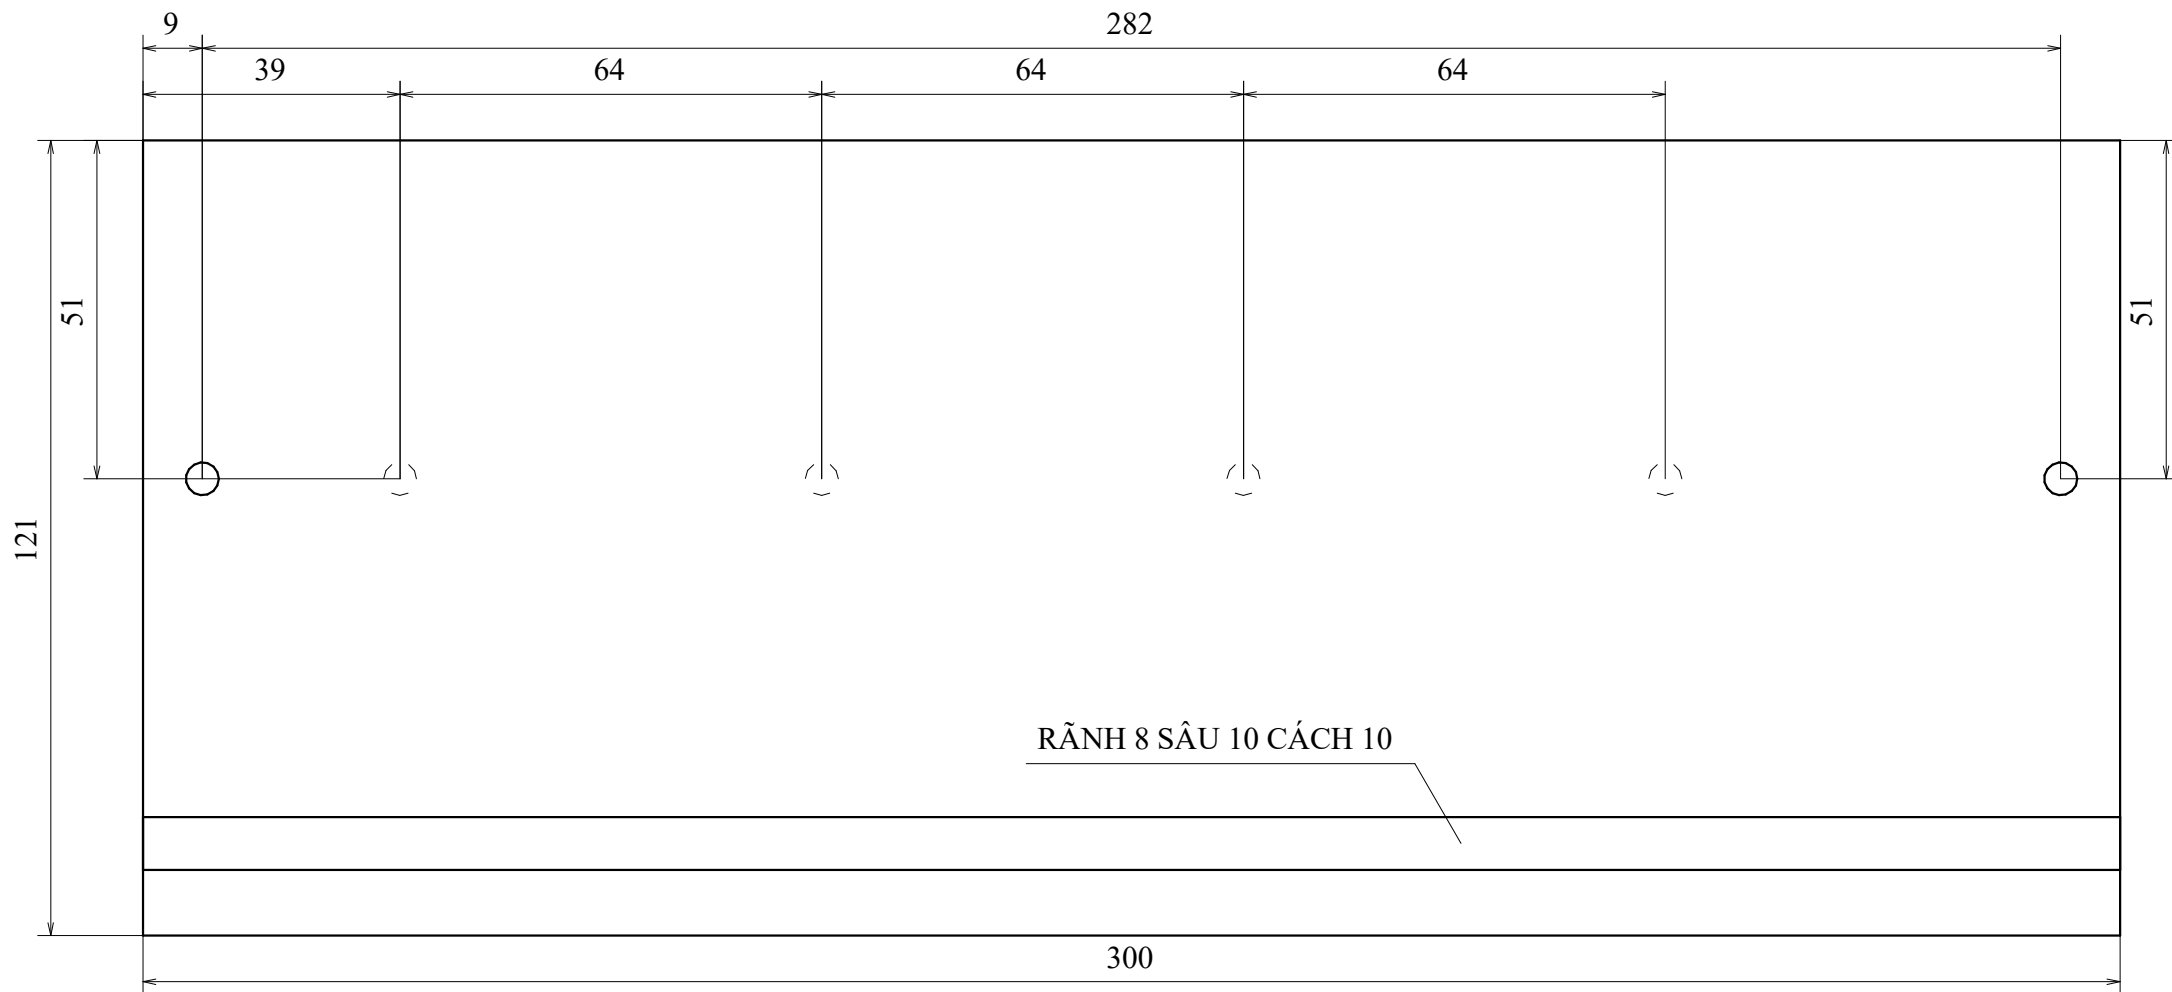

12 . TNK

.SL: 3

Ghi chú

- Ø15 SẤU 13
- ⊗ Ø8 SẤU 13 (MẶT)
- ⊗ Ø8 SẤU 25 (CẠNH)
- ⊗ Ø5 THÙNG

- ⊗ Ø8 THÙNG
- ⊗ Ø8 THÙNG
- ⊗ Ø5 SẤU 13

Dung sai tổng thể ± 5mm

TỦ THẤP (900X350X750)

		Chữ ký	Ngày
Thiết kế	Phạm Huân		07.06.21
Kiểm soát	Văn Nam		
Duyệt			


BẢN VẼ

Vật liệu: OKAL-M1

MBCN ...

Số lượng		

HÒA PHÁT
NHÀ MÁY GỖ HÒA PHÁT

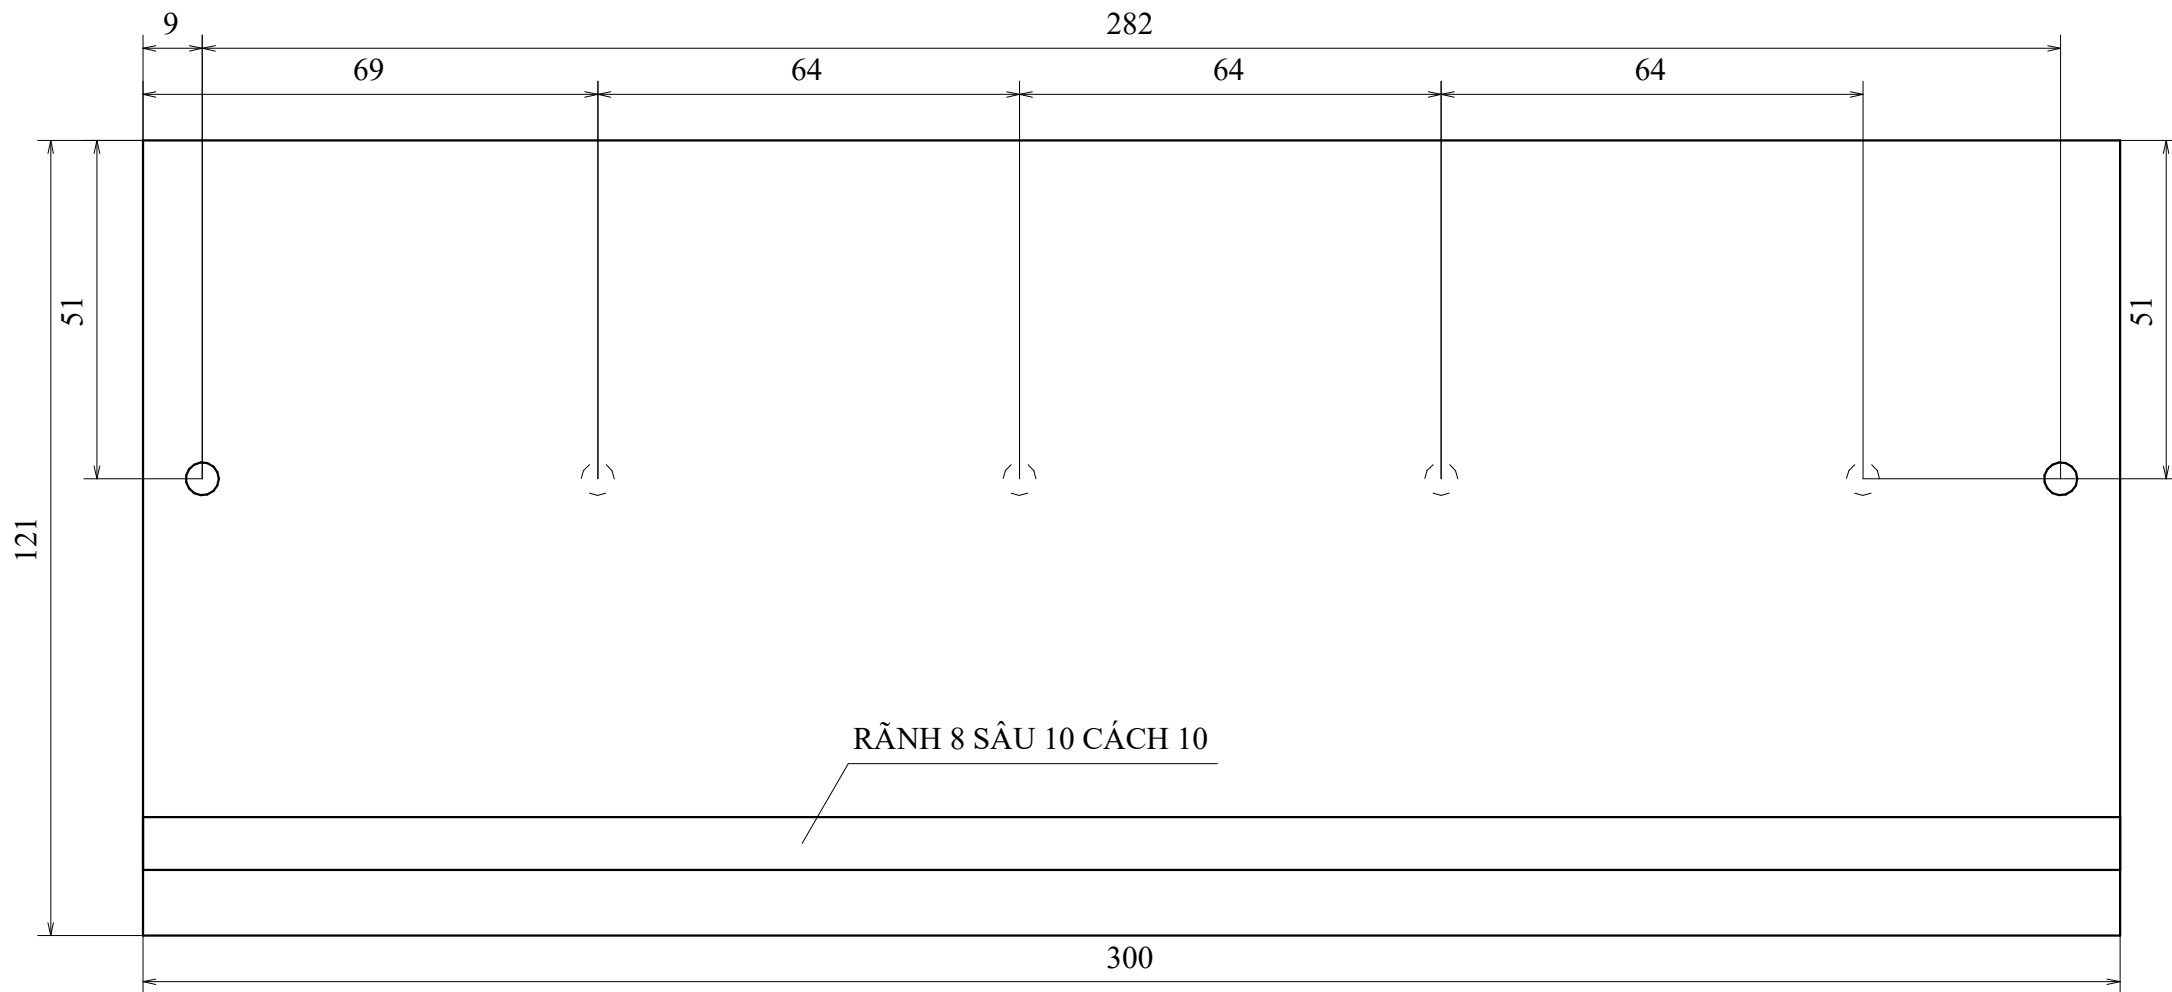

13 . TNK

.SL: 3

Ghi chú

- Ø15 SẤU 13
- ⊗ Ø8 SẤU 13 (MẶT)
- ⊗ Ø8 SẤU 25 (CẠNH)
- ⊗ Ø5 THÙNG

- ⊗ Ø8 THÙNG
- ⊗ Ø8 THÙNG
- ⊗ Ø5 SẤU 13

Dung sai tổng thể ± 5mm

TỦ THẤP (900X350X750)

		Chữ ký	Ngày
Thiết kế	Phạm Huân		07.06.21
Kiểm soát	Văn Nam		
Duyệt			


BẢN VẼ

Vật liệu: OKAL-M1

MBCN ...

Số lượng		

HÒA PHÁT
NHÀ MÁY GỖ HÒA PHÁT

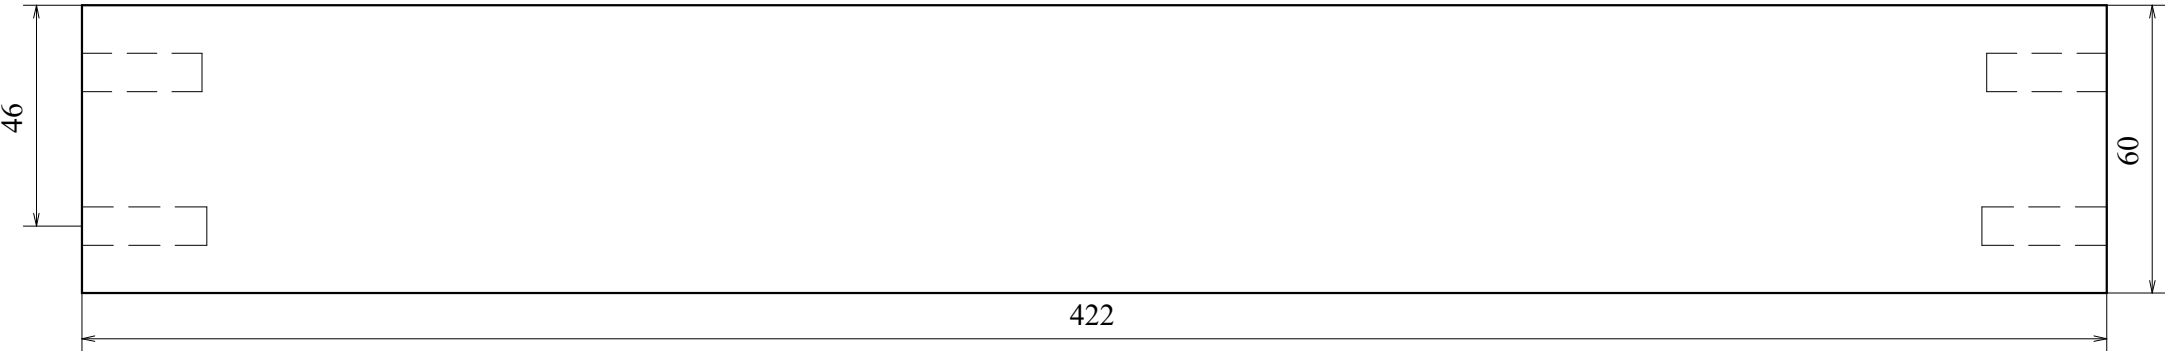

14 . CHAN CON .SL: 2

Ghi chú				TỦ THẤP (900X350X750)							
○ Ø15 SẤU 13 ⊘ Ø8 SẤU 13 (MẶT) ⊘ Ø8 SẤU 25 (CẠNH) ⊗ Ø5 THÙNG	⊗ Ø8 THÙNG ⊗ Ø8 THÙNG ⊕ Ø5 SẤU 13					BẢN VẼ	MBCN ...				
							Số lượng				
				Chữ ký	Ngày						
		Thiết kế	Phạm Huân		07.06.21						
		Kiểm soát	Văn Nam								
		Dung sai tổng thể ± 5mm		Duyệt				Vật liệu: OKAL-M1	 HOA PHAT NHÀ MÁY GỖ HOA PHAT		